




جهاز مدينة القاهرة الجديدة

كتيب الاشتراطات البنائية

مقدمة من جمعية مطوري القاهرة الجديدة



الارتدادات:

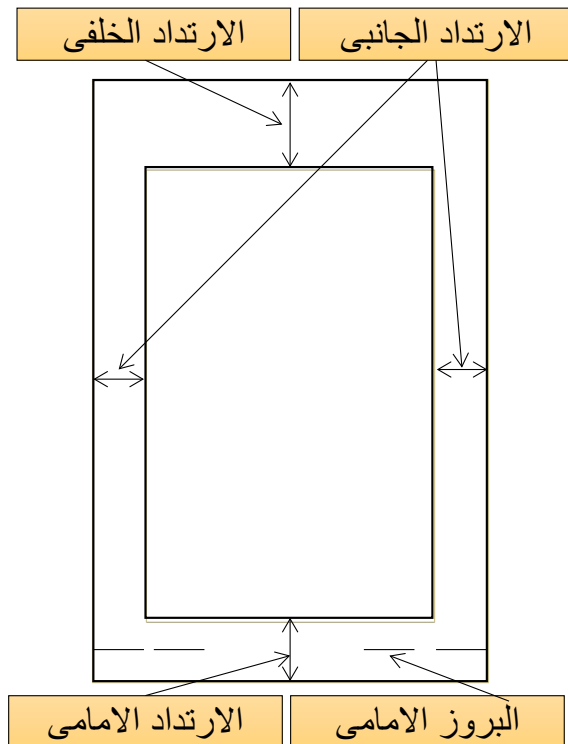

منطقة بيت الوطن:

- الامامي: ٣,٠٠ م.
- الخلفي: ٤,٠٠ م.
- الجانبي:

- واجهه اقل من ٢٠ م: يكون ٢,٥٠ م عدا مدخل الجراج
- لا يقل عن ٣,٠٠ م.
- واجهه ٢٠ م فأكثر: يكون ٣,٠٠ م.

مناطق النرجس الجديدة، شمال الرحاب، جنوب السويس و الاوركيد والنورث هاوس:

- الامامي: ٣,٠٠ م.
- الخلفي:

- ٤,٠٠ م للقطع التي تستوفي النسب البنائية.
- ٣,٠٠ م للقطع الغير مستوفيه النسبه البنائية.

الجانبي:


- ٣,٠٠ م للقطع التي تستوفي النسب البنائية
- ٢,٥٠ م للقطع الغير مستوفيه النسبه البنائية.

النسبة البنائية:

- الدور الارضي **50%** من مساحة الارض.
- الدور المتكرر **55%** من مساحة الارض.
- غرف السطح **25%** من مساحة الدور الأرضي.
- عدد الأدوار:
 - بدروم
 - ارضي
 - ٣ أدوار متكررة
 - غرف سطح
- «المنور لا يدخل ضمن النسبة البنائية»

الرووف	12.5%
المتكرر	55%
المتكرر	55%
المتكرر	55%
الارضى	50%
البدروم	100%


يتم احتساب النسب البنائية طبقا لبصمة الاعمده وحرمها حتى لو كان العمود خارج المبنى
- في حالة عمود ملتصق مع رامب لا يتم احتسابه داخل النسبة البنائية .

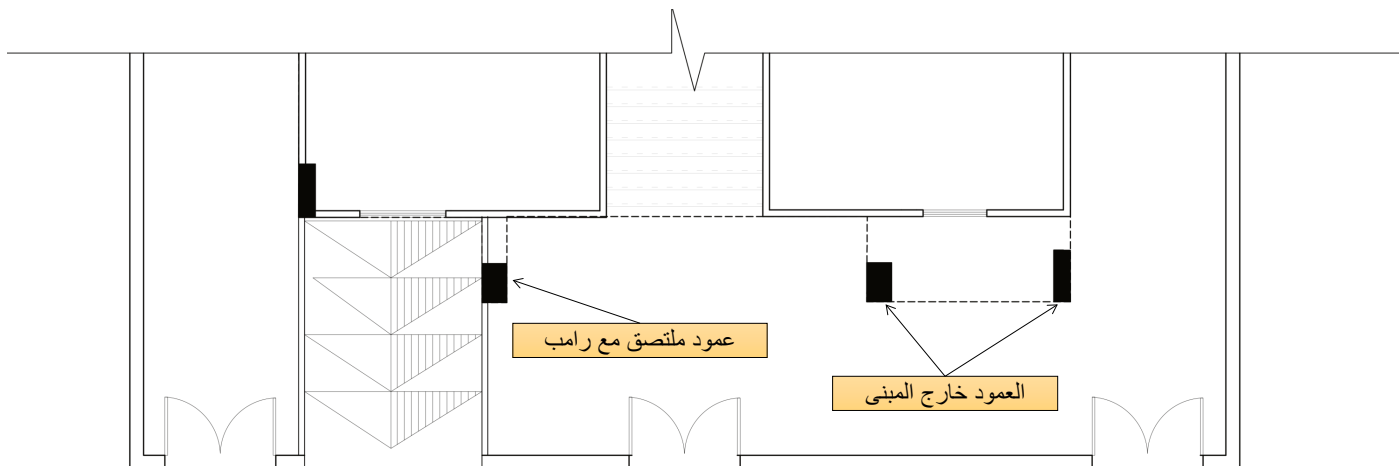

التراسات:

الواجهة الامامية:


- يسمح بعمل تراسات داخل الارتداد الامامي بحد اقصى ١,٢ متر بالأدوار المتكررة فقط مع الالتزام باقل بعد عن حدود الارض ١,٨٠ م.
- لا تقل نسبة التراسات بالواجهة الامامية عن ٥٠% من طول الواجهة.
- لا تزيد نسبة الأبراج بالواجهة الامامية عن ٥٠% من طول الواجهة.
- يتم احتساب مساحات التراسات ضمن المساحة البنائية مساحة كاملة.

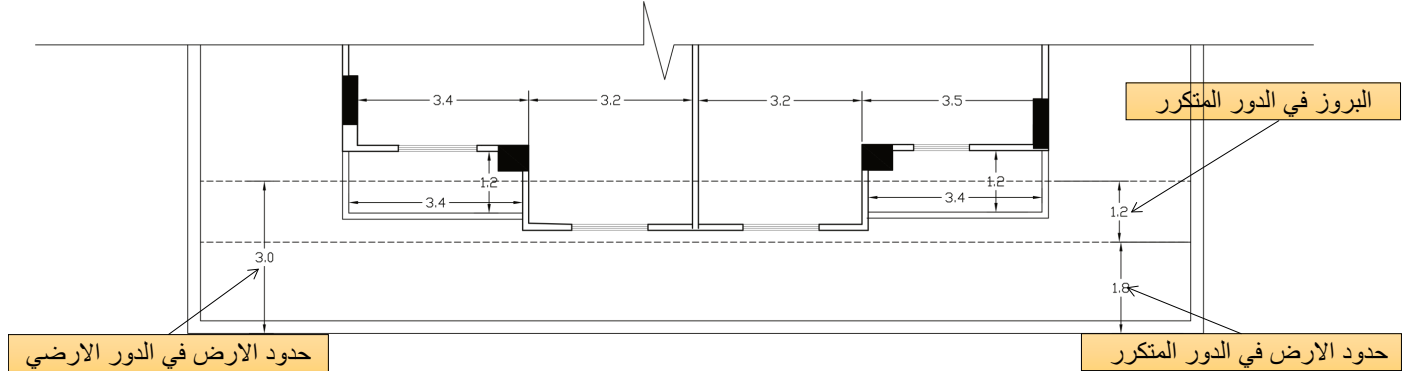


التراسات:

الواجهات الجانبية والخلفية:

- لا يسمح بعمل تراسات داخل الارتدادات.
- يمكن عمل تراسات داخل المساحة البنائية.
- يتم احتساب مساحات التراسات ضمن المساحة البنائية مساحة كاملة.
- يتم عمل التراسات الخلفية المكشوفة في الدور الأرضي و اعتبارهم من النسبة البنائية للأرض.

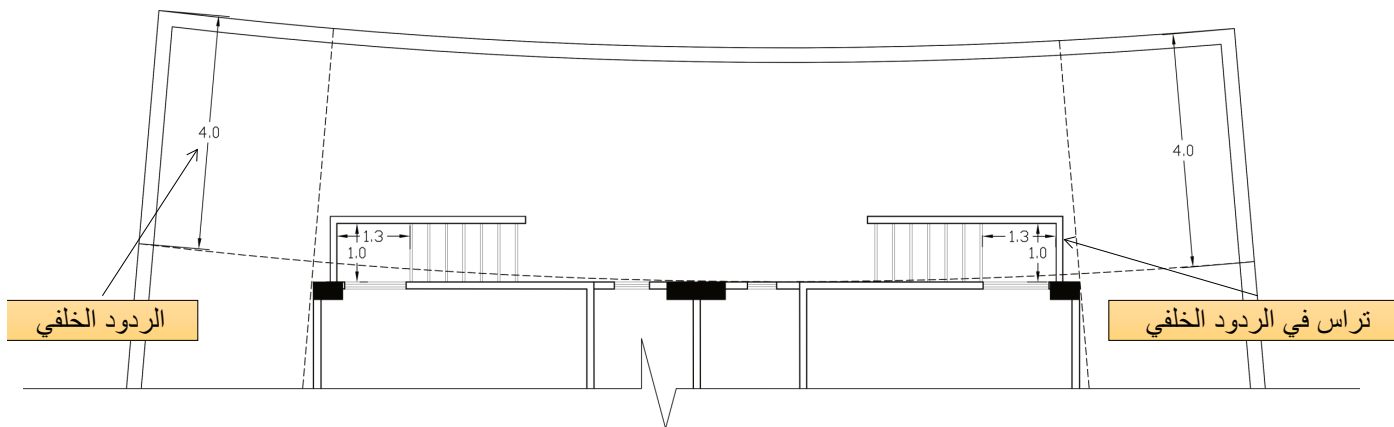


البروز على الممرات عرضها اكثر من ٦,٠٠ م يكون ١٠ سم لكل متر من عرض الممر بحد اقصى ١,٠٠ م لاجمالى البروز .
البروز على الحوائق يكون بحد اقصى ١,٠٠ م .

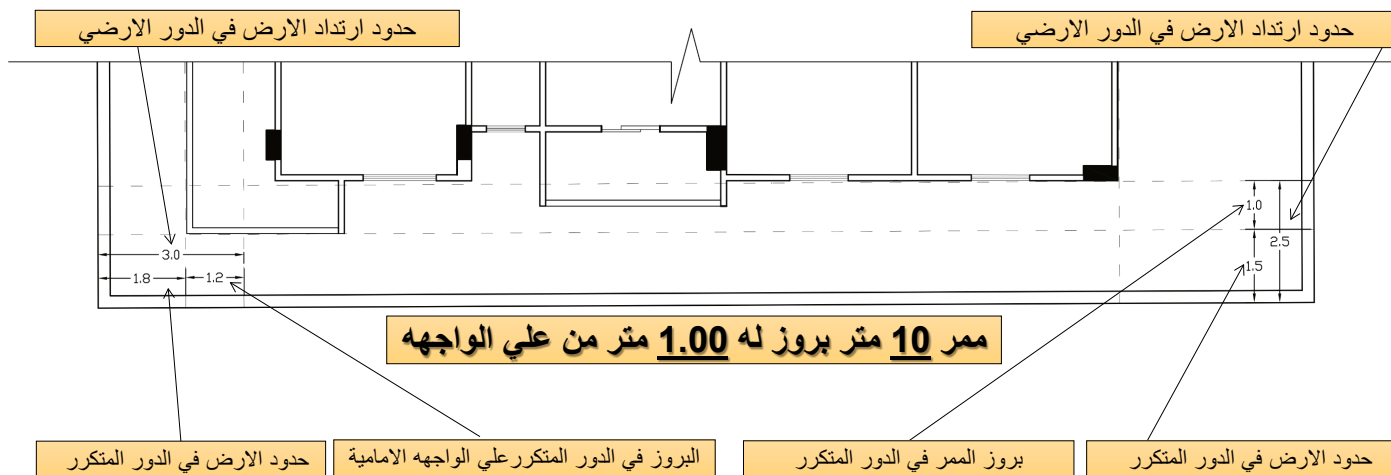

البدروم:

الرامب:


- لا يقل عرض الرامب عن ٣,٠٠ متر.
- مدخل الجراج من الواجهة لا يقل طوله عن ١٠,٠٠ م بداية من حدود الارض.
- مدخل الجراج من داخل المبنى لا يقل طوله عن ٤,٥٠ م بداية من حدود الارض حتي دور الارضي.
- في حالة **اكثر من ٨ وحدات** يتم **عمل رامبين للبدروم** و **فرق بين الرامبين ٨,٠٠ م**.
- في حالة مساحة الجراج **اقل من ٢٥٠ متر مربع** يتم **عمل رامب واحد**.
- في حالة مساحة الجراج **اكبر من ٢٥٠ متر مربع** يتم **عمل رامبين**.

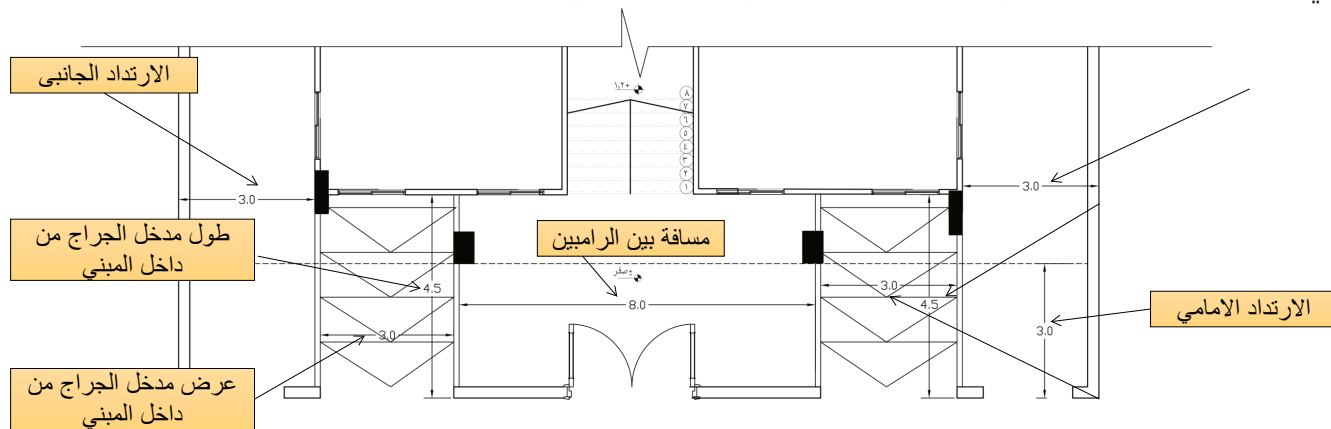

البدروم:

الرامب:


- في حالة الواجهه اقل من ٢٠ م :

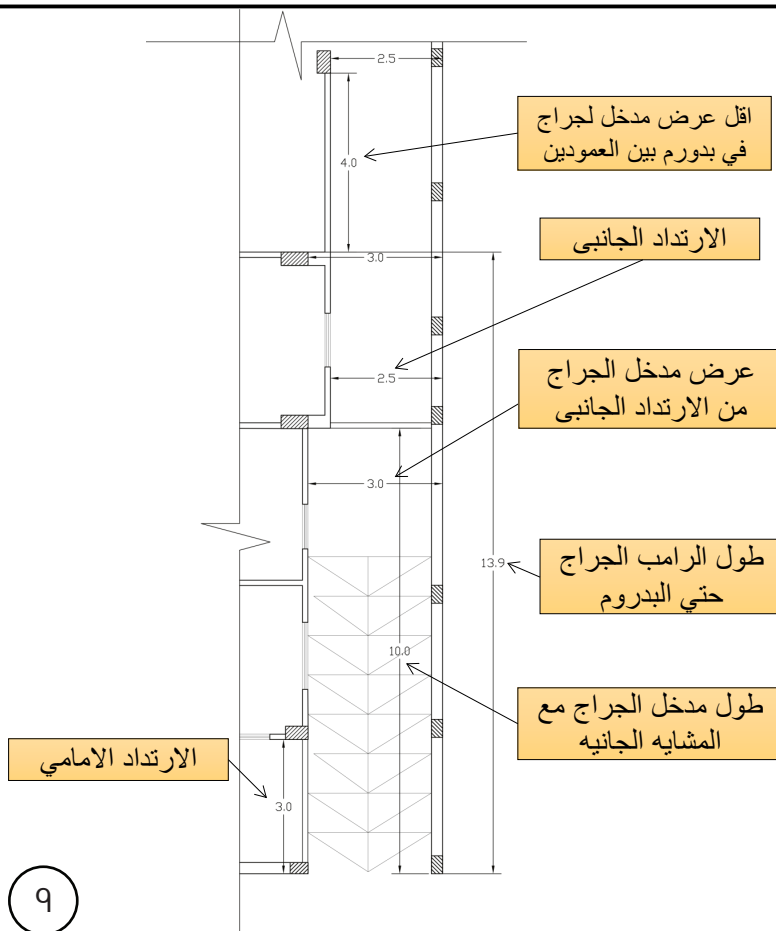


البدر وم:

الجراج:

- لا تقل إبعاد موقف السيارة الواحدة عن ٢,٥ م × ٤,٠ م
- الاستخدام الرسمي (بارك - مخازن - حارس - حمام - صالة ألعاب - خدمات).

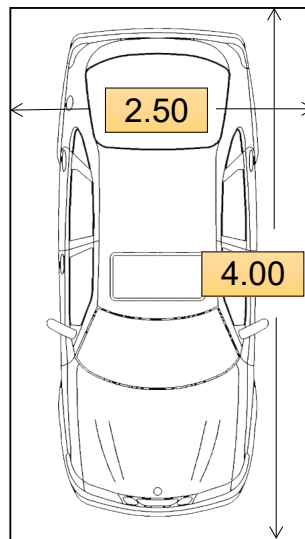


ابعاد موقف السيارة

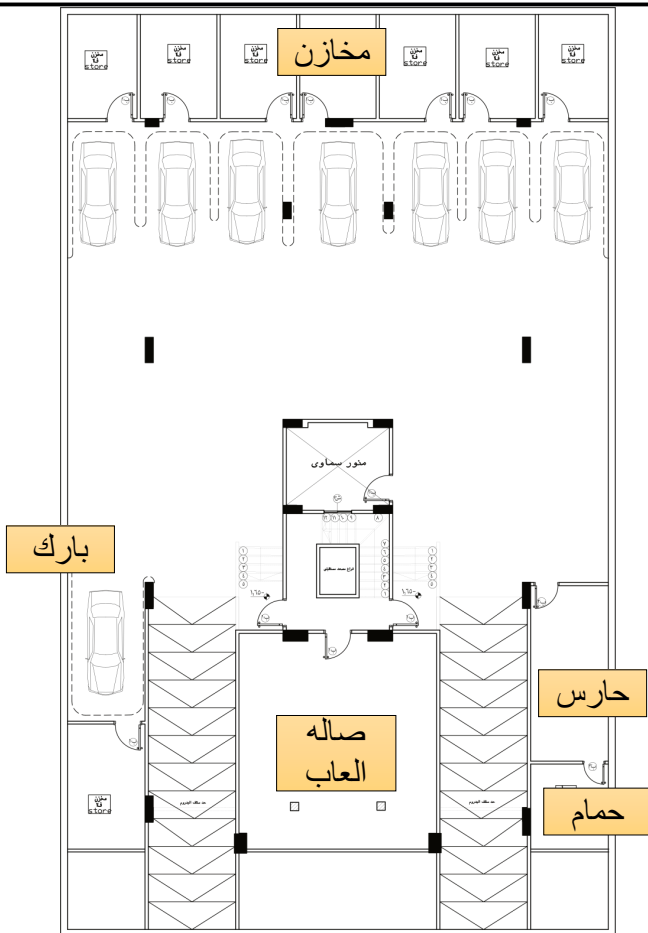

الارتفاعات و المناسيب:


- منسوب الدور الارضي: (+ ٢٠,٢٠م) من الصفر المعماري
- منسوب دور البدر: (- ٢٠,٤٠م) من الصفر المعماري
- ارتفاع الدور المتكرر: ٣,٢٠م
- ارتفاع السور: ٢,٥م من الصفر المعماري.
- منسوب المشايات الجانيه يكون هو نفس منسوب الصفر المعماري ولا يزيد فى حالة وجود فرق منسوب.

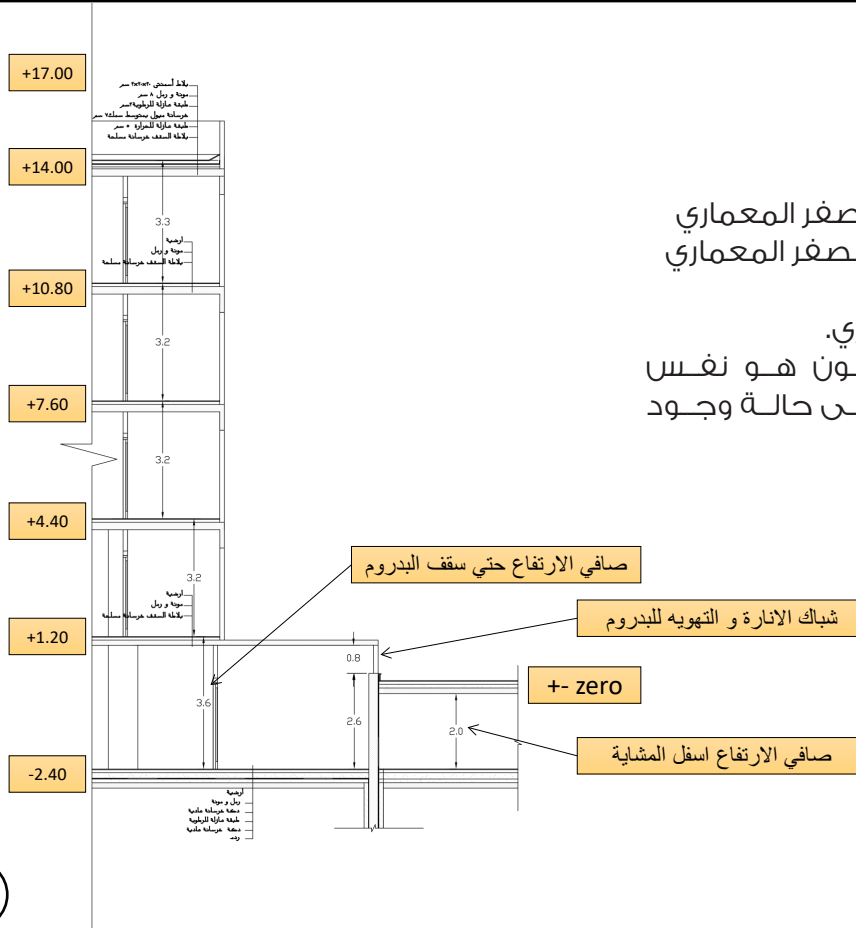


- منسوب المشايات الجانبيه يكون هو نفس منسوب الصفر المعمارى ولا يزيد فى حالة وجود فرق منسوب.
- فرق المنسوب (قيمه معينه يتم اضافتها لمنسوب الارضى فقط طبقا لحالة الموقع على الطبيعه والحد الاقصى له ٧٥ سم ليكون الحد الاقصى لمنسوب الارضى ١,٩٥ م ومصرح به اذا كان الشارع الامامى لقطعة الارض اقل من الخلفى او الجانبى).
- منسوب الصفر المعمارى يكون هو بردورة الرصيف وليس الاسفلت او ظهر بلاعة الصرف .
- فرق المنسوب للقطعه المطلوبه = فرق المنسوب بين الشارع الخلفي و الامامي / ٤ مع افتراض فرق المنسوب بين الشارعين مثلا ٢,٢٠.

$$0.55 = 2.20/4$$

- منسوب الدور الارضى ١,٢٠ + ٠,٥٥ = ١,٧٥ م


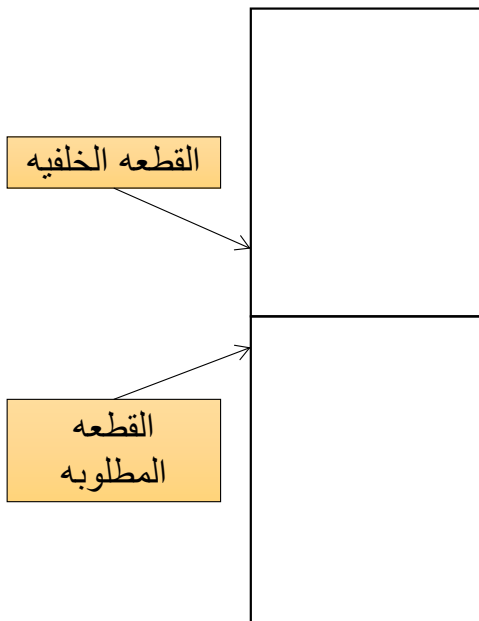


احتساب الصفر المعماري:

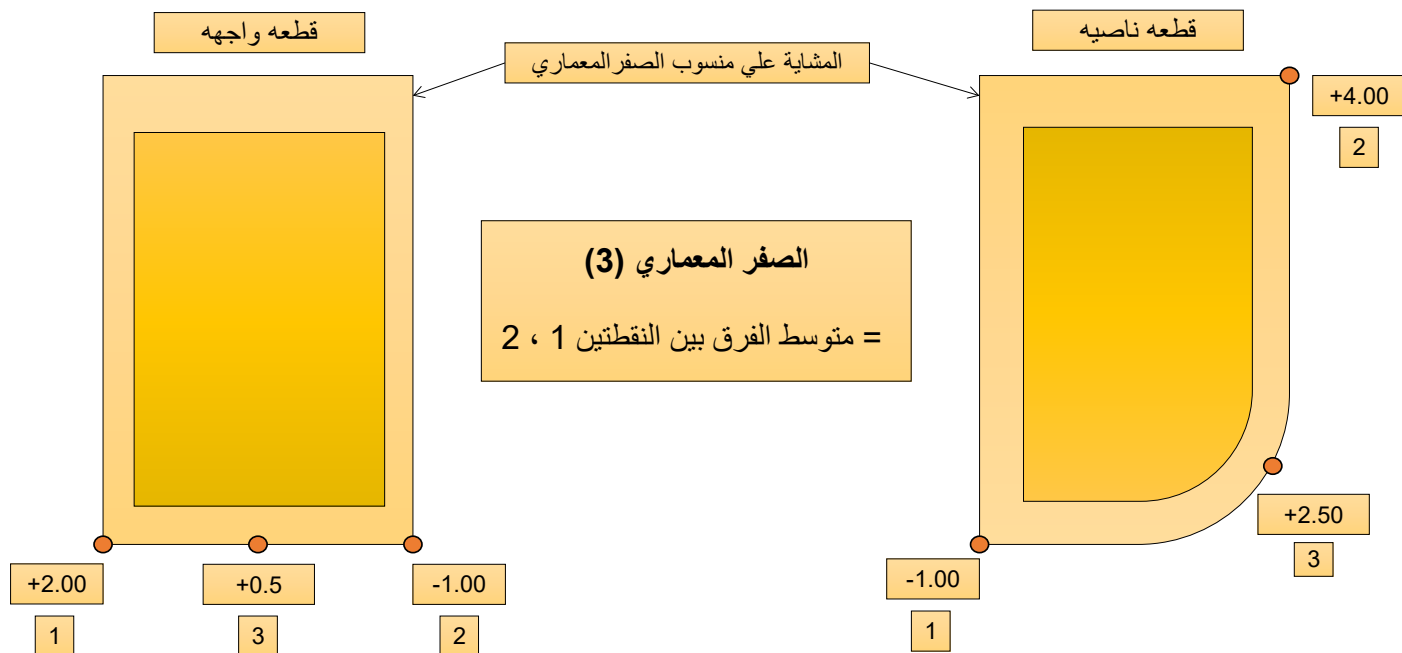


المنور:

- مساحته لا تقل عن 1.0 متر مربع.
- لا يقل اصغر ضلع فيه عن 2.5 متر
- أي خلع أو جيب سواء كان في المنور أو على أي ضلع لا يزيد طوله عن ضعف عرضه.

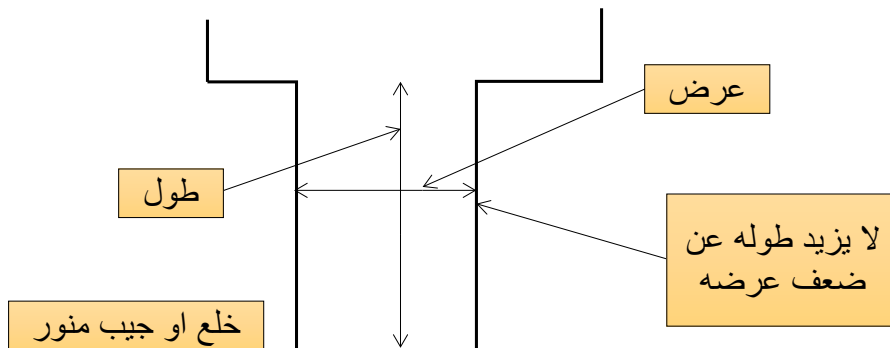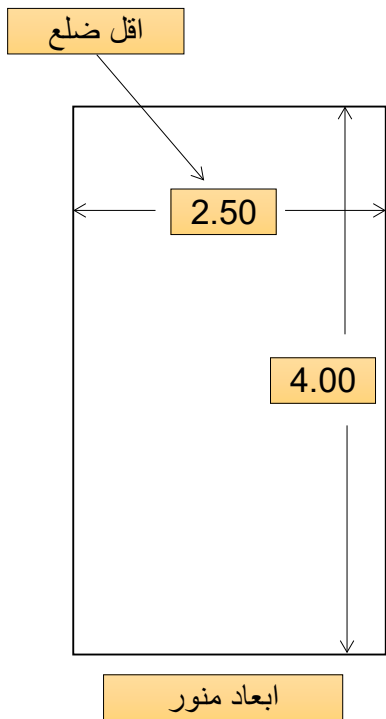


ارتفاعات السور:

- ارتفاع الحطة الاولى للأسوار ٢,٥ متر.
- ارتفاع الحطة الثانية للأسوار ٢,٥ متر.

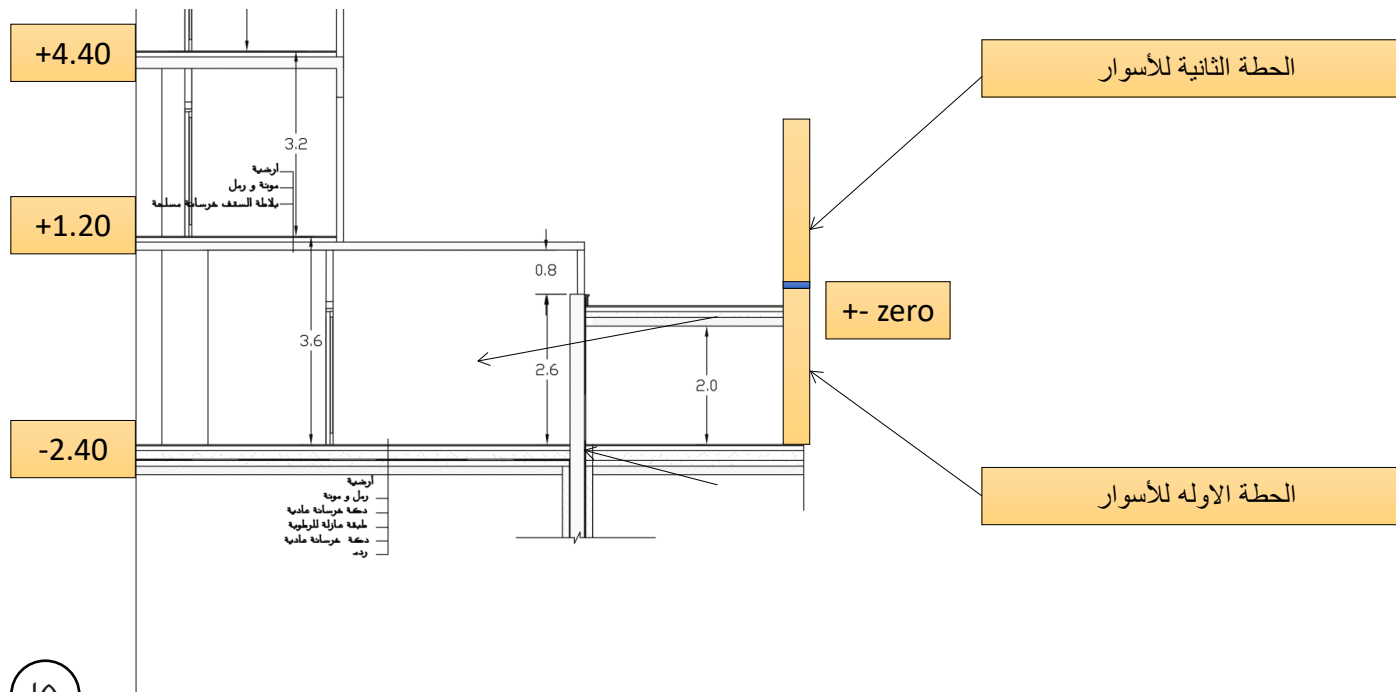


الرووف (السطح):

- الاستخدام الرووف : (خدمات - مخازن - مربيه - غسيل).
- النسبة البنائية : غرف السطح ٢٥٪ من مساحة الدور الأرضي .
- منسوب : (+١٤,٢٠) م من الصفر المعماري .
- «في حالة عمل ممر يجب ان يكون مسقوف»

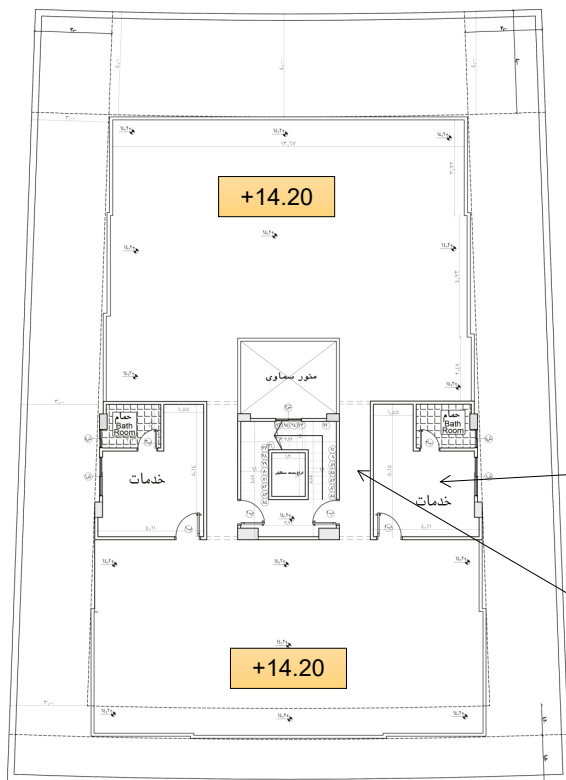

- خدمات
- مخازن
- مربيه
- غسيل
- حمام


ممر مسقوف

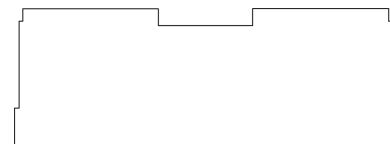


النسبة البنائية

السلم:


سلم علي الواجهه

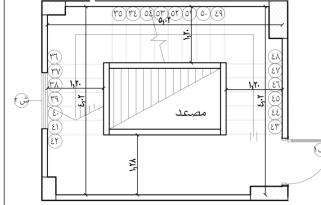

سلم علي منور واحد

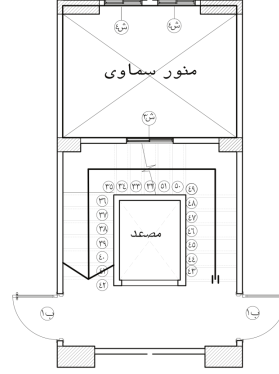

سلم علي منورين

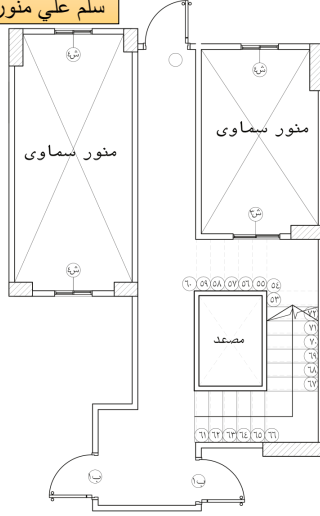


• لابد من وجود مصدر تهويه للسلم سواء منور او يتم سحبه على اى واجهه وهذا يتم تطبيقه للقطع التى لا تحقق نسبه بنائية.

• عرض قلبة السلم لا تقل عن ١,١٠ م ويفضل عملها ١,٢٠ م .

• عرض البسطه امام الشقق لا تقل عن ١,٢٠ م .


• عرض الدرج النائم (لا يقل عن ٢٨ سم وارتفاع الدرج) القائم (لا يزيد عن ١٧

سم)

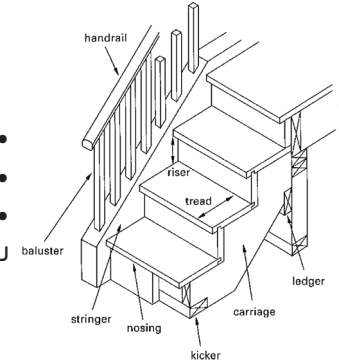

الحليات:


- يسمح بعمل بروزات (حليات او كرانش) لا تتعدى ٣٠ سم على الواجهة.

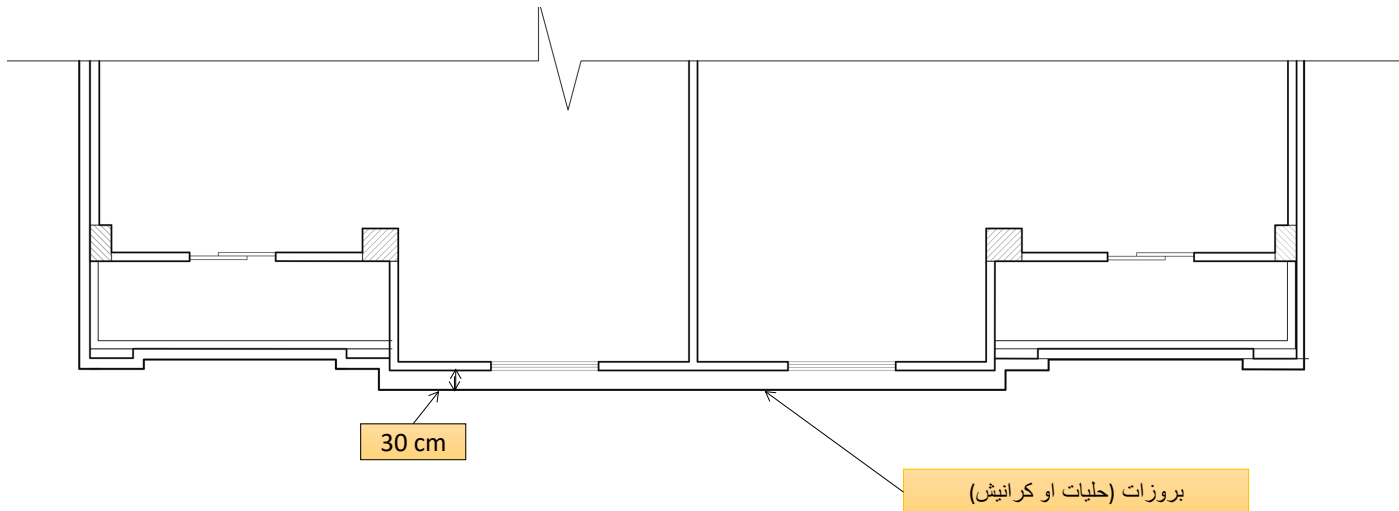



حمام سباحة:

- يسمح بعمل حمام سباحة بعد ١,٥٠ م من حد الارض .
- يسمح بعمل حمام سباحة بعيدا عن القواعد المسلحة لمبني .
- مساحته لا تقل عن ١٠ متر مربع .
- «في حالة عمل بدروم مشترك يجب عمل حمام السباحة في ارتداد احد القطعتين وليس في الجزء المشترك بين القطعتين».

المسقط الافقي المعماري

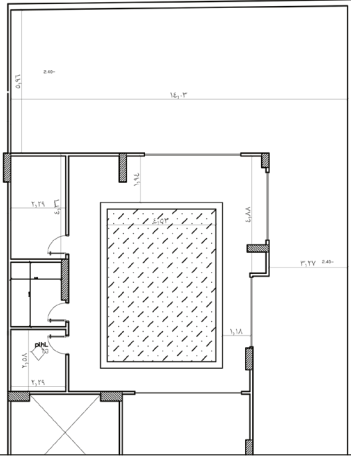

المسقط الافقي الانشائي

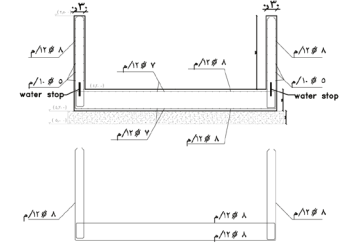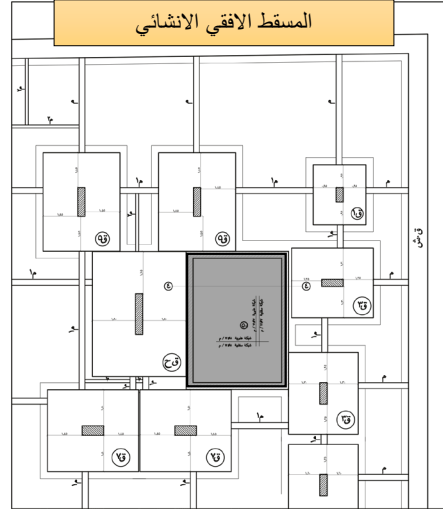


قطاع الحمام السباحه

سور المشترك بين القطعتين:

- يجب الاحتفاظ بالارتداد المبني كما هو.
- عمل سور مشترك بعرض ٢٥ سم.

صافي الارتداد الجانبي في حاله السور منفصل

الارتداد الجانبي

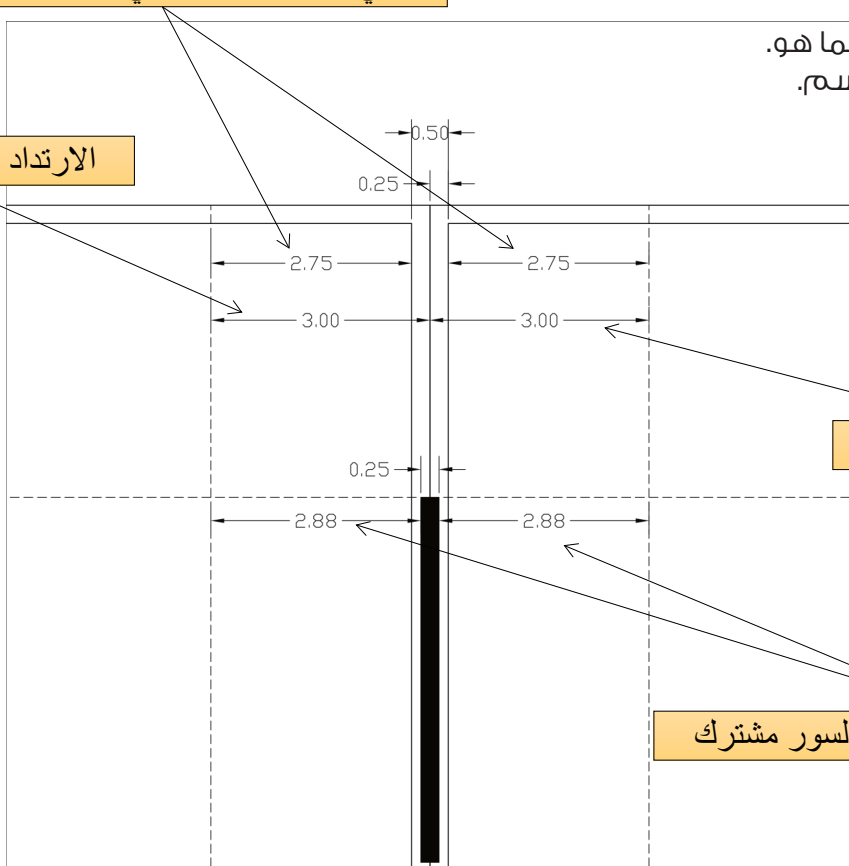

الارتداد الجانبي

صافي الارتداد الجانبي في حاله السور مشترك

المصعد:

أبعاد غرفة الماكينات			السرعات	أبعاد فتحات الأبواب بالسـم		أبعاد الصاعدة بالسـم		أبعاد البئر بالسـم		الحمولة بالأشخاص
إرتفاع	عمق	عرض		إرتفاع	عرض	عمق	عرض	عمق	عرض	
300	300	250	سرعة أو سرعتين	215	100	110	80	150	140	4
300	350	300	سرعتين	215	100	135	100	180	160	6
300	350	300	سرعتين	215	100	135	120	180	185	8

ترتيب اللوحات:

المعماري	الانشائي
المسقط الافقي البدورم	المحاور و الاعمده
المسقط الافقي الارضي	الاساسات
المسقط الافقي المتكرر	تسليح سقف المشايه
المسقط الافقي الرووف	تسليح سقف البدورم
الواجهه الاماميه	تسليح سقف الارضي
الواجهه الخلفيه	تسليح سقف المتكرر
الواجهات الجانبيه	تسليح سقف الرووف
موقع عام	التفاصيل
قطاع	

شكل خرطوشة اللوح المعماريه:


[illegible]

جدول مقاسات الاجواب		
المواصفات	المقاسات	
	عرض	ارتفاع
باب خشب حشوات ارو	١,٠٠	٢,٢٠
باب خشب حشوات ارو	٩٠	٢,٢٠
باب خشب حشوات ارو	٨٠	٢,٢٠
باب خشب حشوات ارو	٧٠	٢,٢٠
باب مدخل كريتال ضلعتين	٢,١٠	٢,٢٠
باب مدخل كريتال ضلعتين	١,٥٠	٢,٢٠
باب تراس الويمتال ضلعتين مثلث	١,٢٠	٢,٥٠
باب مدخل الويمتال ضلعتين	١,٥٠	٢,٢٠
باب اسانيدور ضلعة مفصل	١,١٠	٢,٢٠
باب مدخل الويمتال ضلعتين	٢,١٠	٢,٢٠
باب مدخل كريتال ضلعتين	٣,١٠	٢,٢٠

جدول مقاسات الشباب			
المواصفات	المقاسات		ملاحظات
	ارتفاع	عرض	
الوسات خلفتين منزلق للنوم والاستقبال	١,٢٠	١,٥٠	١ ش
الوسات خلفتين منزلق للنوم والاستقبال	١,٠٠	١,٢	٢ ش
الوسات خلفتين منزلق للسلم	١,٥٠	١,٠٠	٣ ش
الوسات خلفتين منزلق للحمام والمطبخ	٨٠	٨٠	٤ ش
الوسات للحمام	٦٠	٦٠	٥ ش

جدول التشطيبات الداخلية			
الاسقف	الحوامل	الارضيات	الوزرات
دهانات بلاستيك	دهانات بلاستيك	بلاط سيراميك مقاس ١٥,٠×١٥,٠	وزرة سيراميك
دهانات بلاستيك	بلاط سيراميك مقاس ٣٠,٠×١٥,٠	بلاط سيراميك مقاس ١٥,٠×١٥,٠	وزرة سيراميك
لا يوجد	دهانات بلاستيك	بلاط زوايكو مقاس ١٥,٠×١٥,٠	وزرة موزايكو
دهانات زيت	رخام مقاس ٣٠,٠×١٥,٠	ترصيعات رخام مقاس ١٥,٠×١٥,٠	وزرة رخام
دهانات بلاستيك	لا يوجد	بلاط سيراميك مقاس ١٥,٠×١٥,٠	وزرة سيراميك
دهانات بلاستيك	دهانات بلاستيك	خرسانة فيلوكوتر	لا يوجد

عمارة سكنية 		
المالك 		
اسم الوحدة 	رقم الوحدة 	
تصميم الشالي 	رسموات نظيرية 	تصميم معماري
SCALE 0 1 2 1:50 DATE 		

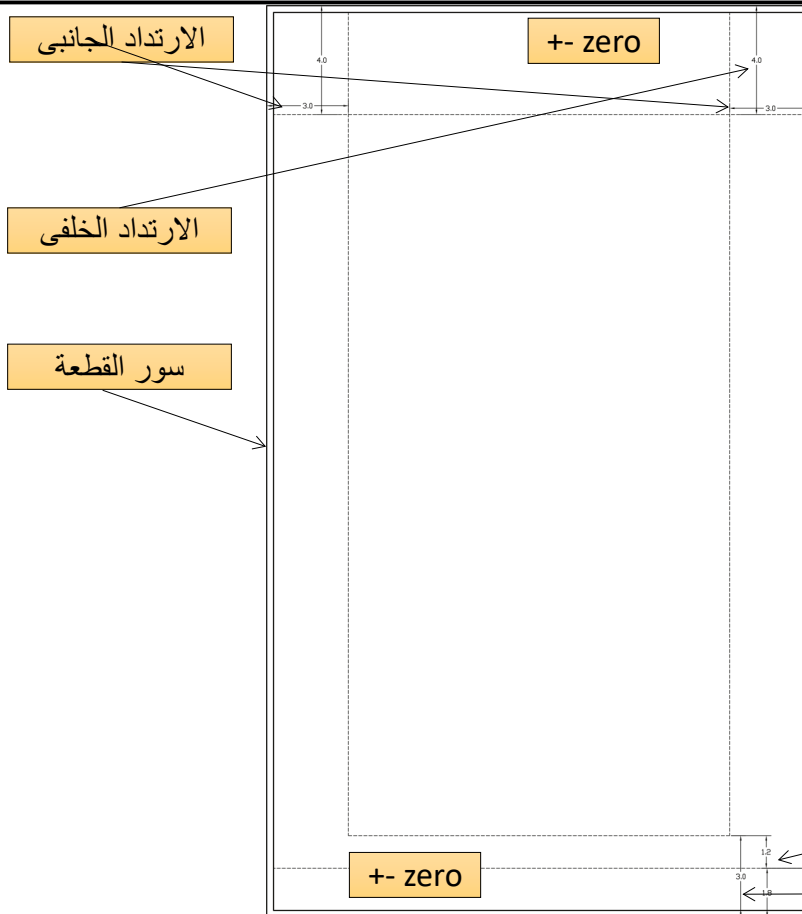

اسس التصميم قبل البدء في المشروع:

- الارتدادات
- المناسيب
- سور القطعة

«ملاحظات عامة»

- المساحة الصافية للوحده لا تقل عن ١٢٠ م^٢.
- عرض المدخل الرئيسي لا يقل عن ٢,٢٠ م.
- عرض البوابة الرئيسية لا يقل عن ١,٨٠ م.
- غرف النوم لا يقل البعد الاصغر فيها عن ٣,٠٠ م.
- عرض البسطة امام الشقق لا تقل عن ١,١٠ م.
- عرض الممرات الداخليه لا يقل عن ١,١٠ م.
- عرض امام التراس لا يقل عن ١,٢٠ م.
- عرض الحمام الرئيسي لا يقل عن ١,٥٠ م.
- عرض حمام الضيوف لا يقل عن ١,١٠ م.
- عرض الاستقبال لا يقل عن ٣,٢٠ م.

«الفهرس»

الموضوع	رقم الصفحة
• الارتدادات	٠٢
• النسبة البنائية	٠٣
• التراسات (الواجهة الامامية)	٠٥
• التراسات (الواجهات الجانبية والخلفية)	٠٦
• البدروم	٠٨
• الجراج	١٠
• الارتفاعات و المناسيب	١١
• احتساب الصفر المعماري	١٣
• المنور	١٤
• ارتفاعات السور	١٥
• الرووف (السطح)	١٦
• السلم	١٧
• الحلقات	١٨
• حمام السباحة	١٩
• السور المشترك بين القطعتين	٢٠
• المصعد	٢١
• ترتيب اللوحات	٢٢
• شكل خرطوش اللوح المعمارية	٢٣
• اساس التصميم قبل البدء في المشروع	٢٤
• ملاحظات عامة	٢٥